


[3] Project Architecture

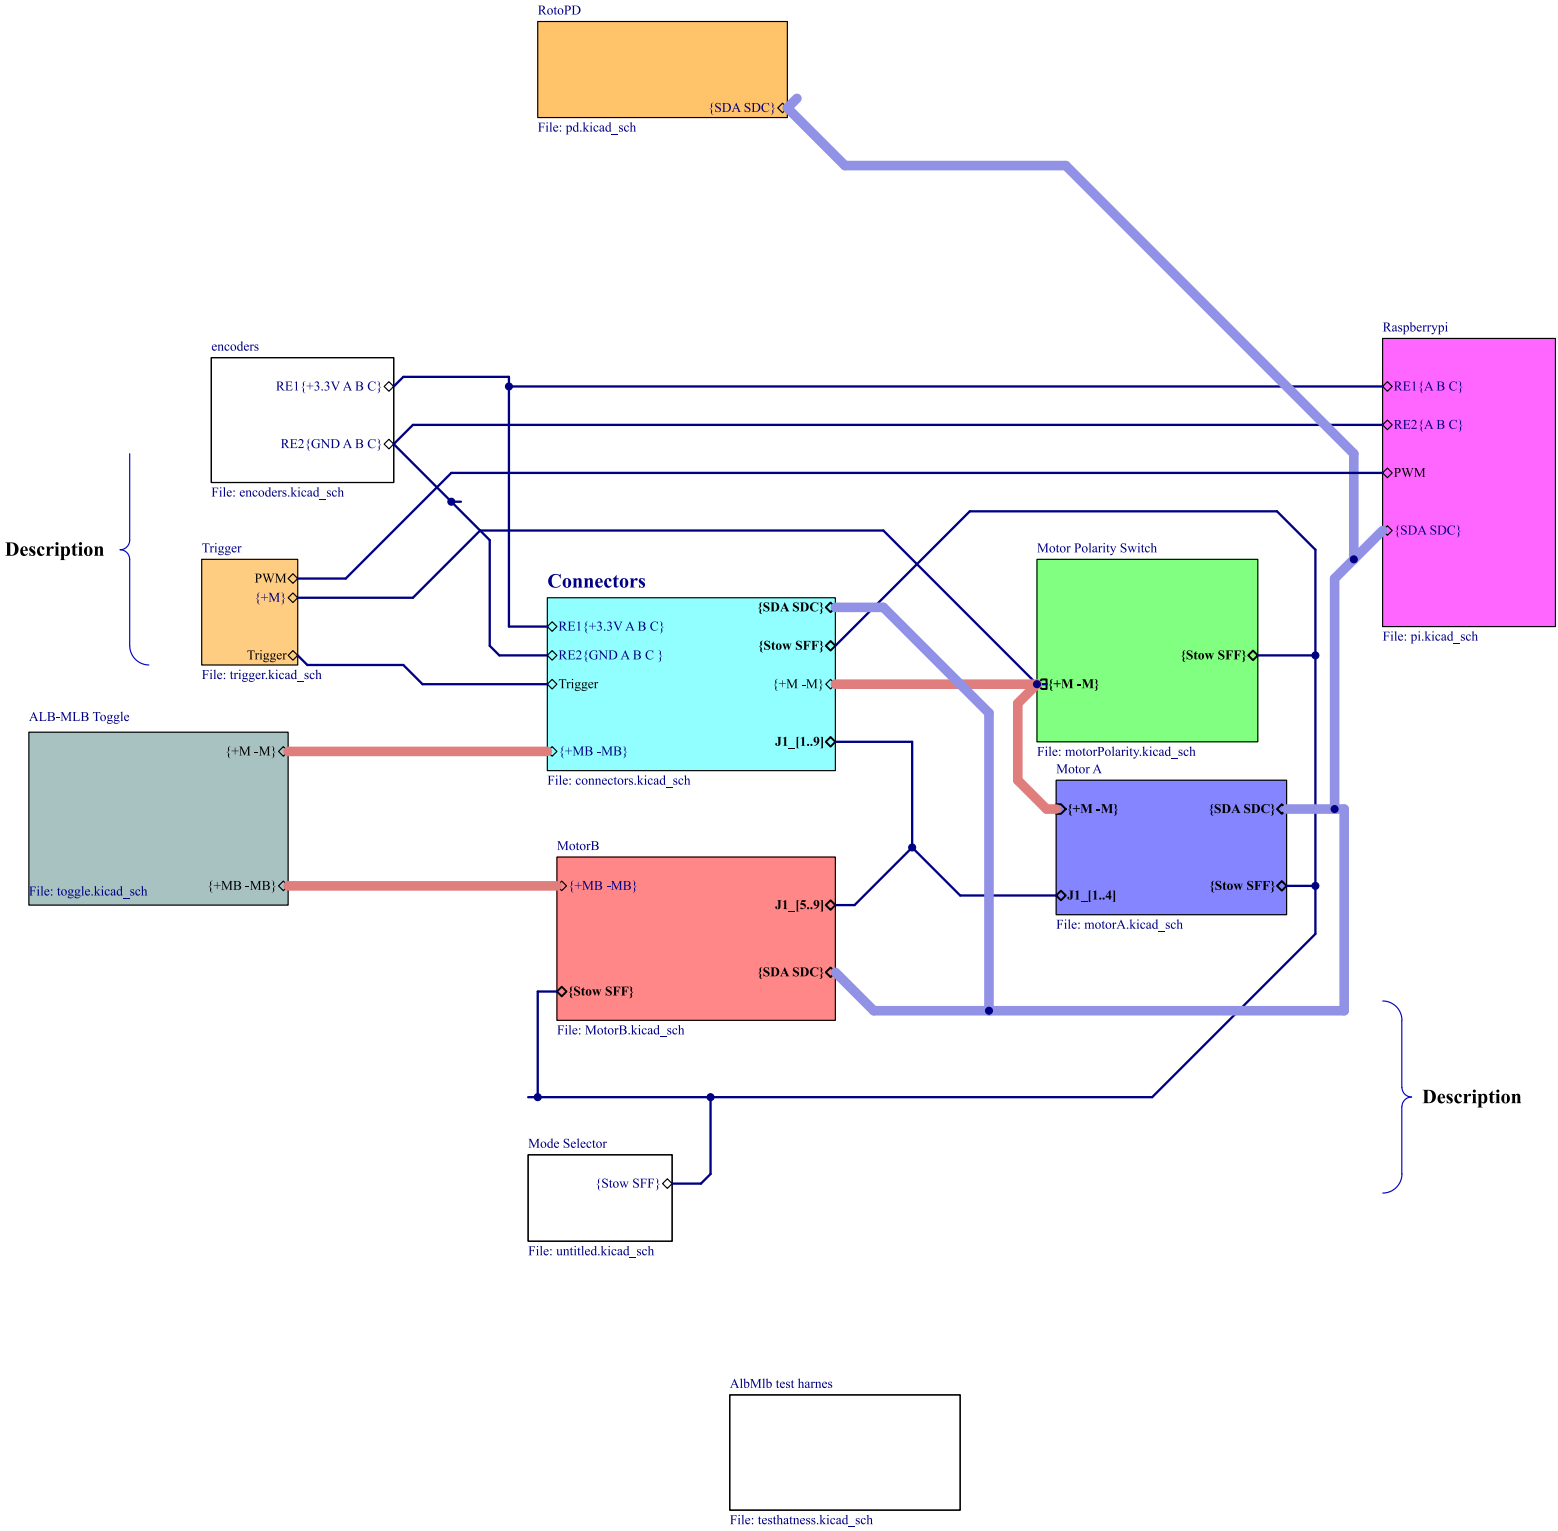

	Comments:	Company: General Atomics EMS		Variant: PRELIMINARY	Git Hash: d2a9a5a
		Board Name: LightBandit		Project Name: LightBandit	
	Sheet Title: Project Architecture	File Name: Project Architecture.kicad_sch	Designer: Marcus Reighter	Date: 2025-01-12	Revision: + (Unreleased)
Sheet Path: /Project Architecture/			Reviewer:	Size: A3	Sheet: 3 of 16